


2350x1500 Воздух-Воздух (ВА)

№	Наименование	Сортамент	Размер	Шт.	Примечание
1	Труба	60х40	2430	2	
2	Труба	60х40	1500	2	
3	Труба	60х40	140	4	
4	Труба	60х40	680	2	
5	Труба	60х40	2350	2	
6	Труба	60х40	720	5	
7	Швеллер	60х40	720	3	
8	Петля строповочная	220х140	-	4	
9	Швеллер	60х40	414.4	14	Срез

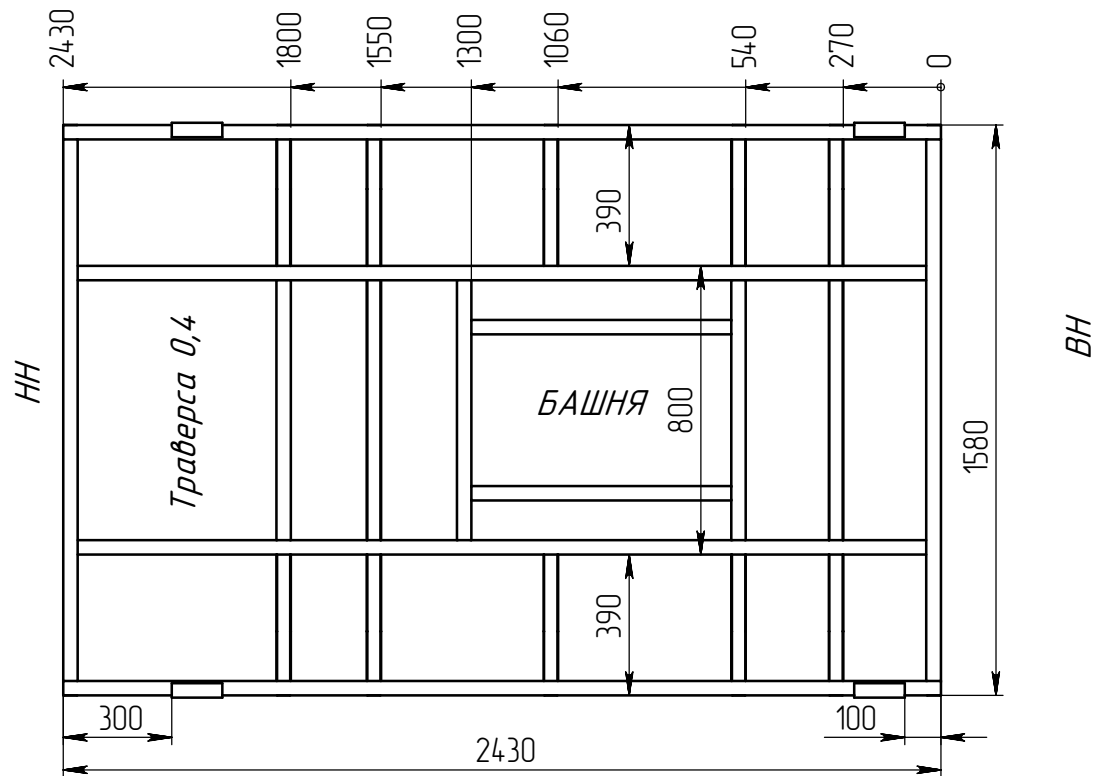

1. Настил крыши должен быть выполнен из стали толщиной 2-мм

Изм.	Лист	№ докум.	Подп.	Дата

2350x1500 Воздух-Воздух (ВА) (ПКТ)


Лист
4

Копировал


Формат А3

Файл: Сборка22

2350x1500 Воздух-Воздух (ВА)

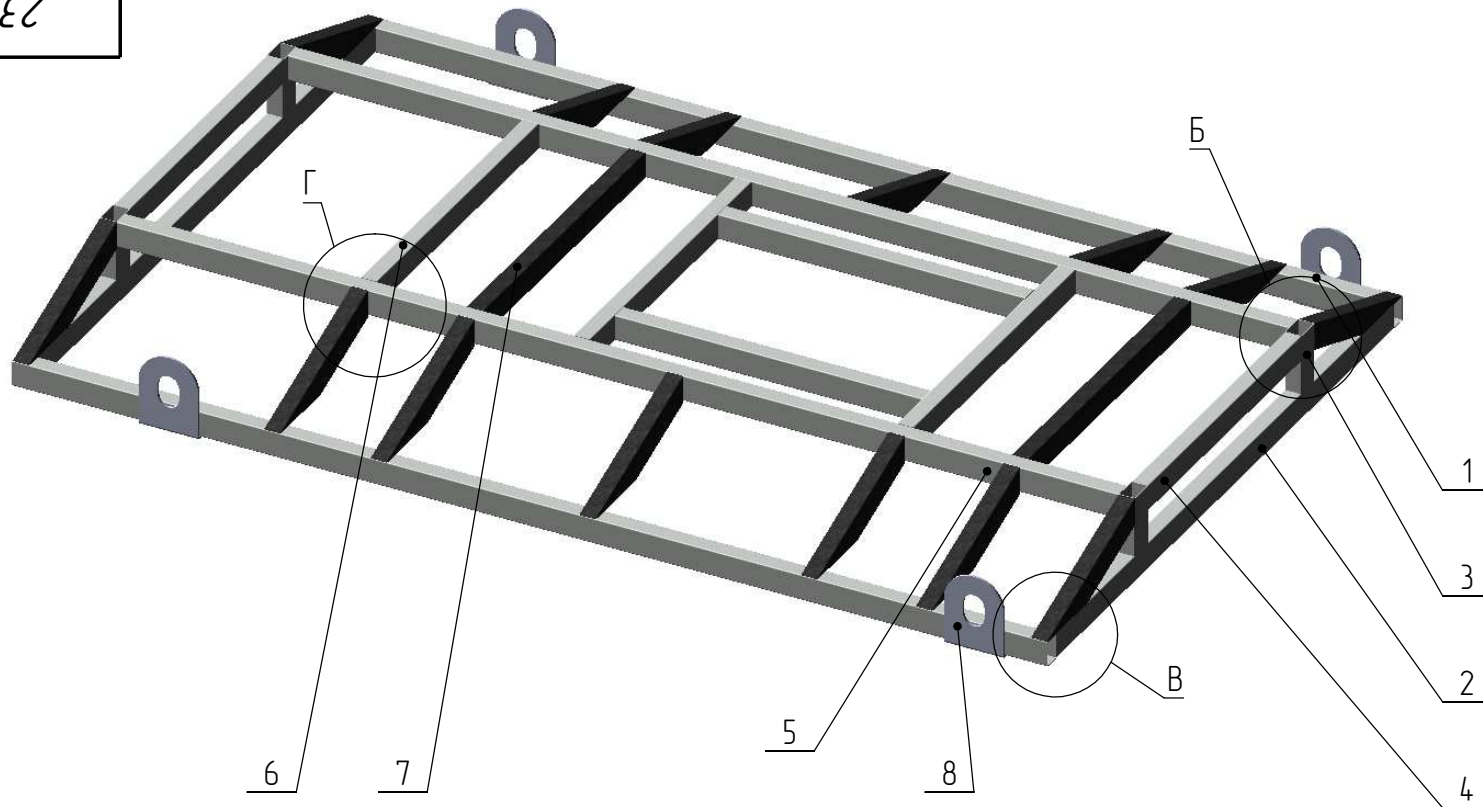


ВИД Г
1:5

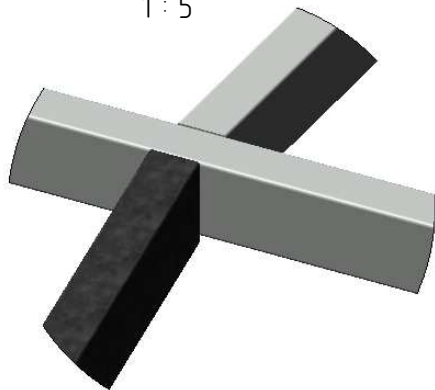

ВИД Б
1:5



ВИД А
1:5

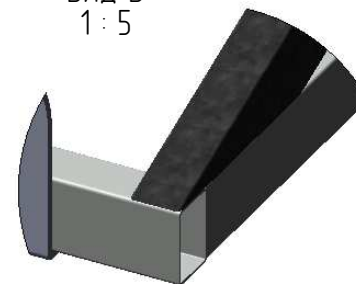

Изм.	Лист	№ докум.	Подп.	Дата

2350x1500 Воздух-Воздух (ВА) (ПКТ)

Лист
5

Копировал

Формат А3

Файл: Сборка22